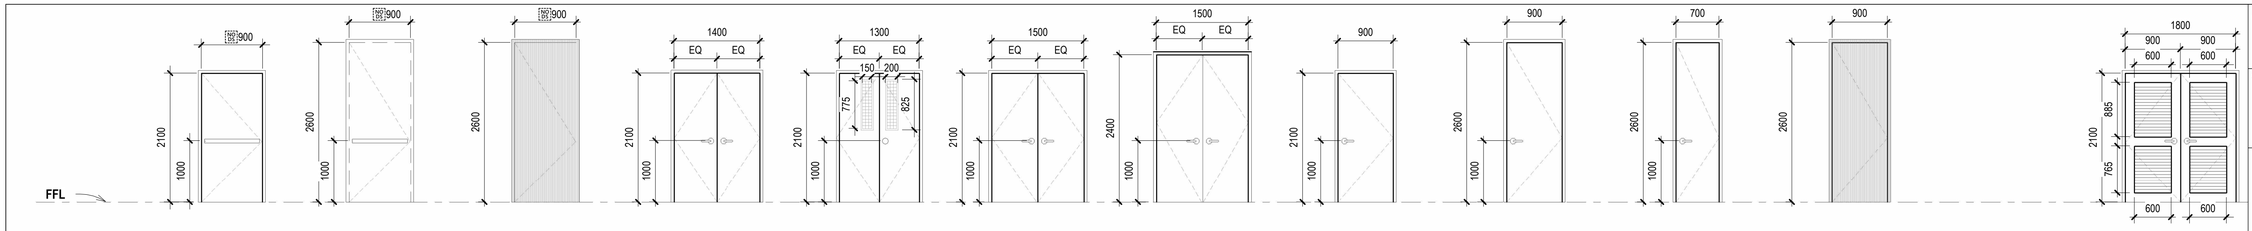

DESIGNATION	SD 01	SD 01A	SD 01B	SD 02	SD 03	SD 04	SD 04A	SD 05	SD 05A	SD 05B	SD 05C		SD 07
DESCRIPTION	SWING TYPE, SINGLE LEAF HOLLOW METAL DOOR & FRAME WITH 2 HRS. FIRE RATING. EPOXY PAINT FINISH	SWING TYPE, SINGLE LEAF HOLLOW METAL DOOR & FRAME WITH 2 HRS. FIRE - RATING. EPOXY PAINT FINISH	SWING TYPE, SINGLE LEAF HOLLOW METAL DOOR & FRAME WITH 2 HRS. FIRE -RATING. CONCEALED DOOR IN CLADDING FINISH.	SWING TYPE, DOUBLE LEAF HOLLOW METAL DOOR & FRAME WITH FIRE - RATING. EPOXY PAINT FINISH	SWING TYPE, DOUBLE LEAF HOLLOW METAL DOOR & FRAME WITH WIRED GLASS VIEW PANEL, FIRE RATED EPOXY PAINT FINISH	SWING TYPE, DOUBLE LEAF HOLLOW METAL DOOR & FRAME. EPOXY PAINT FINISH	SWING TYPE, DOUBLE LEAF HOLLOW METAL DOOR & FRAMES WITH FIRE RATING, EPOXY PAINT FINISH	SWING TYPE, SINGLE LEAF HOLLOW METAL DOOR & FRAME WITH FIRE-RATING. EPOXY PAINT FINISH	SWING TYPE, SINGLE LEAF HOLLOW METAL DOOR & FRAME WITH FIRE-RATING. EPOXY PAINT FINISH	SWING TYPE, SINGLE LEAF HOLLOW METAL DOOR & FRAME WITH FIRE-RATING EPOXY PAINT FINISH	SWING TYPE, SINGLE LEAF HOLLOW METAL DOOR & FRAME WITH FIRE-RATING. CONCEALED DOOR IN CLADDING FINISH.		SWING TYPE, DOUBLE LEAF METAL DOOR AND FRAME, FULLY LOUVERED. EPOXY PAINT FINISH
LOCATION	**BASEMENT 5 TO UPPER DECK** - FES 1 & 2 (RE-ENTRY AT EVERY 4 FLOORS STARTING FROM GROUND FLR.) *(VERIFY DETAILS - F+P DRS-201)*	**LEVEL 2A TO LEVEL 51** - FES 2 (RE-ENTRY AT EVERY 4 FLOORS STARTING FROM GROUND FLR.) *(VERIFY DETAILS - F+P DRS-201)*	**LEVEL 2B TO LEVEL 51** - FES 1	**GROUND FLOOR-** SERVICE ENTRANCE	**BASEMENT 5 TO BASEMENT 2 -** SERVICE LIFT LOBBY *(VERIFY DETAILS - F+P DRS-201)*	**BASEMENT 2, LOWER GROUND FLOOR -** SERVICE LIFT & LOBBY HALLWAY	**LEVEL 2A -** SERVICE LIFT & LOBBY HALLWAY	**BASEMENT 5 TO 1 -** EE ROOM, AIR EXHAUST **BASEMENT 2 -** TELCO ROOM, CATV ROOM **LOWER GROUND -** GAS LINE ROOM, REFUSE STORAGE, GUARD HOUSE, FCC SECURITY ROOM, UNASSIGNED ROOM **LOWER ROOF DECK -** UNASSIGNED ROOM, EE ROOM **UPPER ROOF DECK** - MACHINE ROOM *(VERIFY DETAILS - F+P DRS-201)*	**UPPER GROUND FLOOR TO LEVEL 51 -** SERVICE LIFT LOBBY AND EE ROOM *(VERIFY DETAILS - F+P DRS-201)*	**LEVEL 2B-LEVEL 3 -** MEP SHAFT **LEVEL 5 TO ROOF DECK -** MEP SHAFT *(VERIFY DETAILS - F+P DRS-201)*	**LEVEL 3 TO LEVEL 51** - EE ROOM		**BASEMENT 4 -** DOMESTIC WATER PUMP ROOM **BASEMENT 2 -** RAINWATER PUMP ROOM, MCB ROOM **BASEMENT 1 -** LVSG, PHEX ROOM & COMBINER/MDF ROOM
REMARKS	*WITH DOOR CLOSER. PANIC HARDWARE (VERIFY HARDWARE SCHEDULE)*	*WITH DOOR CLOSER. PANIC HARDWARE (VERIFY HARDWARE SCHEDULE)*	*VERIFY HARDWARE SCHEDULE*	*VERIFY HARDWARE SCHEDULE*	*VERIFY HARDWARE SCHEDULE*	*VERIFY HARDWARE SCHEDULE*	*VERIFY HARDWARE SCHEDULE*	*VERIFY HARDWARE SCHEDULE*	*VERIFY HARDWARE SCHEDULE*	*VERIFY HARDWARE SCHEDULE*	*VERIFY HARDWARE SCHEDULE*		*VERIFY HARDWARE SCHEDULE*

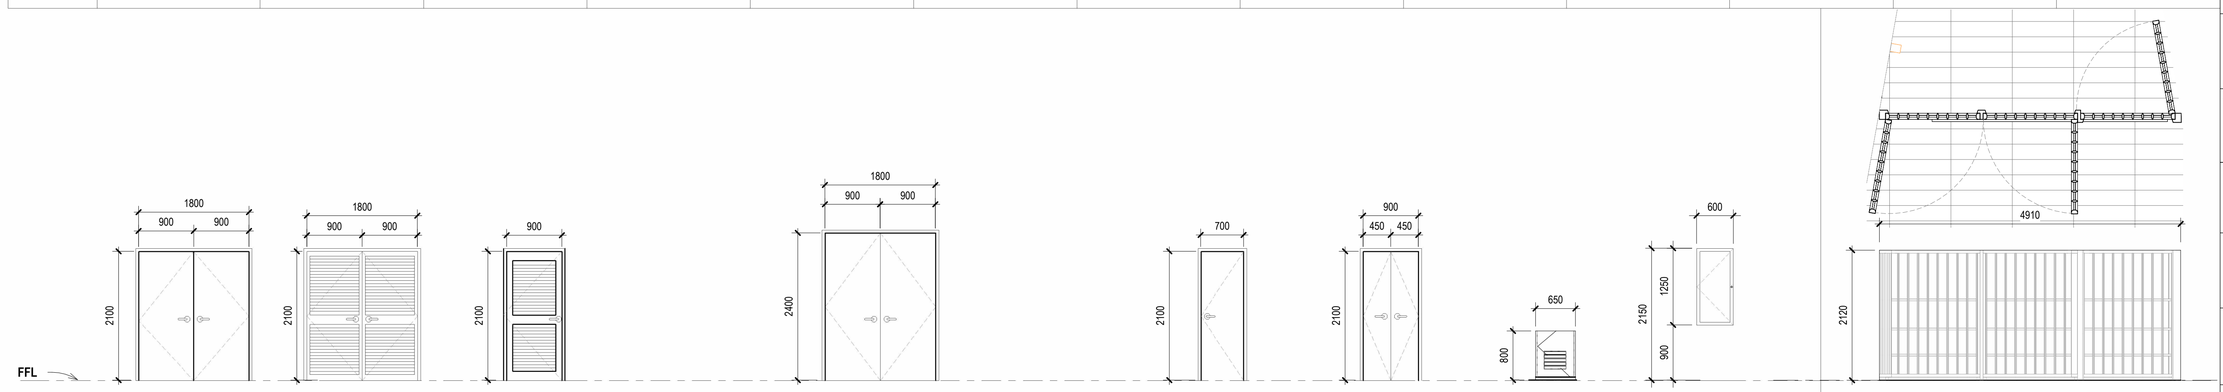

DESIGNATION	SD 07A	SD 07B	SD 07C		SD 09		SD 11	SD 12	SD 13	SD 14	GR 01
DESCRIPTION	SWING TYPE, DOUBLE LEAF HOLLOW METAL DOOR AND FRAME. EPOXY PAINT FINISH	SWING TYPE, DOUBLE LEAF METAL DOOR AND FRAME, STORMED LOUVERED. EPOXY PAINT FINISH	SWING TYPE, SINGLE LEAF METAL DOOR AND FRAME, STORMED LOUVERED. VERIFY MECHANICAL FOR FIRE- RATING. EPOXY PAINT FINISH		SWING TYPE, DOUBLE LEAF HOLLOW METAL DOOR AND FRAME. *VERIFY MECHANICAL REQ'TS FOR FIRE- RATING.* EPOXY PAINT FINISH		SWING TYPE, SINGLE LEAF HOLLOW METAL DOOR & FRAMES. EPOXY PAINT FINISH	SWING TYPE, DOUBLE LEAF HOLLOW METAL DOOR & FRAMES. EPOXY PAINT FINISH	SINGL-LEAF HOLLOW METAL DOOR AND FRAMES WITH LOUVERS ENAMEL PAINTED	SWING TYPE, SINGLE LEAF HOLLOW METAL DOOR & FRAMES. EPOXY PAINT FINISH	SWING TYPE, METAL GRILLE GATE WITH FLOOR SPRING AND MAGLOCK HEAD. EPOXY PAINT FINISH
LOCATION	**BASEMENT 1** - GENSET ROOM	**LOWER GROUND FR -** PMV,MRF **LOWER ROOF DECK -** PUMP ROOM	**LOWER ROOF DECK -** PUMP ROOM		**BASEMENT 1** - GENSET ROOM		**BASEMENT 1 -** AIR-INTAKE PLENUM ACCESS **UPPER GROUND FLOOR** - STORAGE, ACCU ACCESS	**LOWER GROUND FLOOR** - MAINTENANCE ACCESS FOR SLIDING GATE TRACK @ GUARD HOUSE, FCC & SECURITY ROOM	**LEVEL 2B (FACILITIES)** - POOL DECK-MAINTENANCE ROOM	**LEVEL 2B (FACILITIES) - LEVEL 51 -** FES 1	**GROUND FLOOR -** PEDESTRIAN MAIN ENTRANCE / EXIT *(VERIFY DETAILS - F+P DRS-402)*
REMARKS	*VERIFY HARDWARE SCHEDULE*	*VERIFY HARDWARE SCHEDULE*	*VERIFY HARDWARE SCHEDULE*		*VERIFY HARDWARE SCHEDULE*		*VERIFY HARDWARE SCHEDULE*	*VERIFY HARDWARE SCHEDULE*	*VERIFY HARDWARE SCHEDULE*	*VERIFY HARDWARE SCHEDULE*	*VERIFY HARDWARE SCHEDULE*

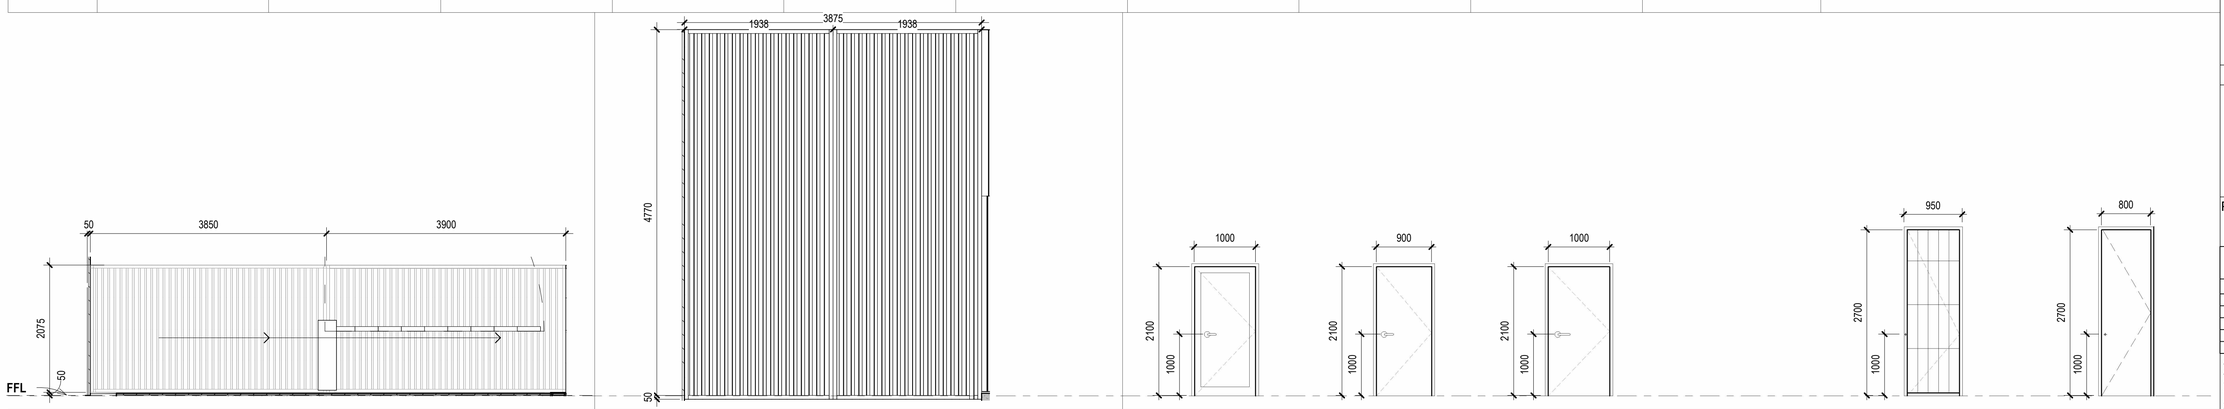

DESIGNATION	GR 02	GR 03		WD 01	WD 02	WD 03		WD 05	WD 06
DESCRIPTION	SLIDING TYPE, GRILLE GATE. FINISH REFER TO FACADE CONSULTANT'S SPECIFICATION	SLIDING TYPE, GRILLE GATE. FINISH REFER TO FACADE CONSULTANT'S SPECIFICATION		SWING TYPE, SINGLE LEAF HOLLOW CORE FLUSHED DOOR IN PAINT FINISH	SWING TYPE, SINGLE-LEAF HOLLOW CORE FLUSH WOOD DOOR AND FRAMES WITH FACES IN PAINTED FINISH	SWING TYPE, SINGLE-LEAF HOLLOW CORE FLUSH WOOD DOOR AND FRAMES WITH FACES IN PAINTED FINISH		SWING-TYPE, SINGLE LEAF SOLID-CORE, FLUSH WOOD DOOR & FRAME. PAINT FINISH	SWING TYPE, SINGLE LEAF SOLID-CORE, FLUSH WOOD DOOR & FRAME. PAINT FINISH
LOCATION	**LOWER GROUND FLOOR -** VEHICULAR MAIN ENTRANCE / EXIT *(VERIFY DETAILS - F+P DRS-401)*	**LOWER GROUND FLOOR** - SERVICE GATE *(VERIFY DETAILS - F+P)*		**LOWER GROUND FLOOR -** DRIVERS AREA, HOUSE KEEPING OFFICE	**LOWER GROUND FLOOR -** FEMALE AND MALE WC, CHANGING ROOM	**LOWER GROUND FLOOR -** STORAGE AREA		**LEVEL 3 -** KITCHEN *(VERIFY DETAILS - F+P DRS-105)*	**LEVEL 5 TO 51** - FAMILY ROOM, MASTER BEDROOM, JUNIOR MASTER BEDROOM AND BEDROOM 1 & 2
REMARKS	*VERIFY HARDWARE SCHEDULE*	*VERIFY HARDWARE SCHEDULE*		*REFER TO I.D. DETAIL & SPECS*	*REFER TO I.D. DETAIL & SPECS*	*REFER TO I.D. DETAIL & SPECS*		*REFER TO I.D. DETAIL & SPECS*	*REFER TO I.D. DETAIL & SPECS*

C+A CONSTRUCTION DRAWING PHASE

PROJECT TITLE
BWDC RESIDENTIAL TOWER
26TH STREET CORNER FORBES TOWN ROAD, BONIFACIO GLOBAL CITY, TAGUIG CITY PHILIPPINES

OWNER
Bonifacio West Development Corporation
GROUND FLOOR MALL FORBES TOWN ROAD BONIFACIO GLOBAL CITY, TAGUIG CITY, PHILIPPINES

ARCHITECT
CASAS+ ARCHITECTS
6th FLOOR, PASEO CENTER, 8757 PASEO DE ROXAS AVENUE, SALCEDO VILLAGE, MAKATI CITY, 1227 PHILIPPINES
TEL. NO. (+632) 8-840-4450
EMAIL: information@casasarchitects.com
GAYLORD S. BONGALON
REG. NO.: 0014648 TIN. 201-200-655
PTR 9565871 ISSUED MAKATI CITY

DESIGN CONSULTANT
Foster + Partners
Riverside, 22 Hester Road
London SW11 4AN
T+44 (0)20 7738 0455
© Foster + Partners 2017

STRUCTURAL
SYQ & ASSOCIATES STRUCTURAL ENGINEERS
9801 Kamagong Street,
Brgy. San Antonio Village Makati City
Telephone No. +(632) 893-41-57
Fax No. 896-97-60 to 61
e-mail address:
info@syqsquared.com

STRUCTURAL CONSULTANT
MAGNUSSON KLEMENCIC ASSOCIATES
Structural + Civil Engineers
Seattle Chicago
1301 Fifth Avenue Suite 3200, Seattle, WA USA
Telephone No: 206 292 1200
Fax No: 206 292 1201
Website: https://www.mka.com/

ELECTRICAL / MECHANICAL / SANITARY & FIRE PROTECTION
MEINHARDT
25TH Floor Chatam House
116 Valero cor. V.A. Rufino St.
Salcedo Village, Makati City
Tels. (632) 887-1391
Fax. (632) 887-1172
E-mail mpi@meinhardt.com.ph

ACOUSTICS/SECURITY CONSULTANT
dB acoustics
23rd Floor Unit F Summer One Tower
530 Shaw Blvd. Metro Manila
Mandaluyong, Philippines
Telephone No. (02) 718 0808
www.08db.com

FACADE CONSULTANT
Front
15/B E-Trade Plaza,
24 Lee Chung Street,
Chai Wan, Hong Kong
Telephone No. +852 5804 9256
Fax No. +852 5804 9257

LIGHTING CONSULTANT
BO STEIBER LIGHTING DESIGN
279 River Valley Road,
FDA Wu Tower
#04-01, Singapore 238320
Telephone No. +65 6219 3329
Fax No. +65 6219 3327
mailto@bsld.com.sg
www.bsld.com.sg

LANDSCAPE CONSULTANT
CRÉARIS
99 Mindanao Avenue
Project 8, Quezon City
1106 Metro Manila
Philippines
Telephone No. (02) 356 4921
Website: crearis-manila.business.site
Email: inquiries@crearis.com.ph

PROJECT MANAGER
design coordinates, inc.
Suite 202, ITC Building,
337 Sen. Gil Puyat Avenue,
Makati City, Philippines
Telephone No. (+632) 8896 1981 to 84
Email: info@dci.com.ph

QUANTITY SURVEYOR
QUANTITY SOLUTIONS
9F Alabang Corporate Center,
W Service Road,Muntinlupa 1780
Telephone No. (+632) 8-856-7700
Fax No. (+632) 8-856-1744
Email: info@quantitysolution.com

KEYPLAN

KEY SECTION

PACKAGE NAME:
CONTRACT DOCUMENTS

REVISIONS

REV NO	DATE	DESCRIPTION

All measurements are to be verified on site by contractor. All discrepancies are to be immediately reported to the architects and project / construction managers. Contractors are to prepare and submit shop drawings to architects prior to commencement of works. Ther drawings acting as an instrument of service is the property of CASAS+ ARCHITECTS and cannot be reproduced without their written consent RA 9266.

SHEET CONTENTS
DOOR SCHEDULE

SIGNED BY:		SHEET NO. :
DRAWN BY:	JP/AT/RG/CA/CP/CC	A-0901
CAD BY:		
CHECKED BY:	JM/MR/JP	
DATE DRAWN:	20 SEP 2024	
DATE PRINTED:	20 SEP 2024	JOB NO.:2017-0905