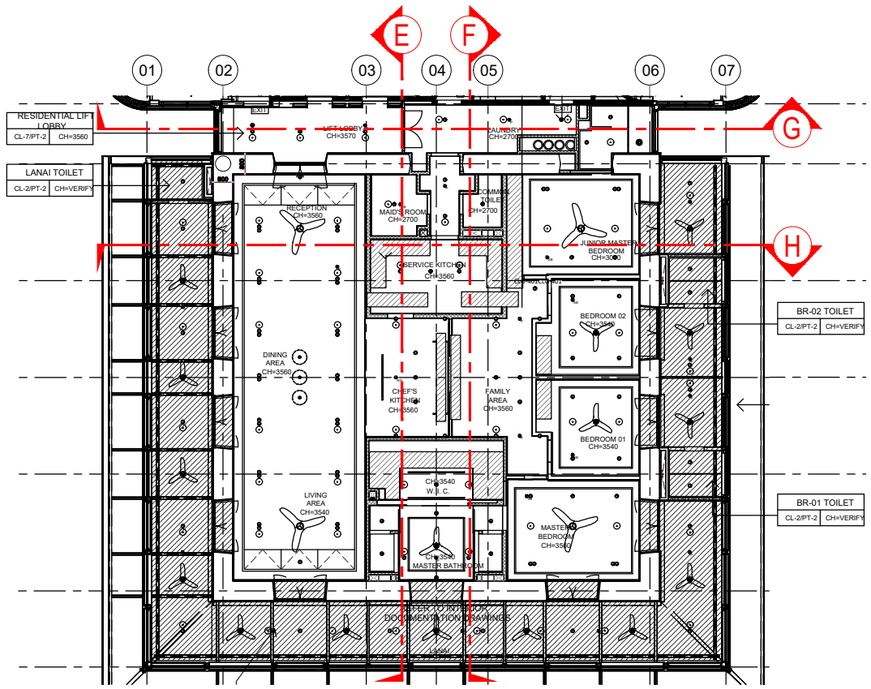

LEVEL 17
RCP PLAN
1 SD-2 SCALE 1:250M

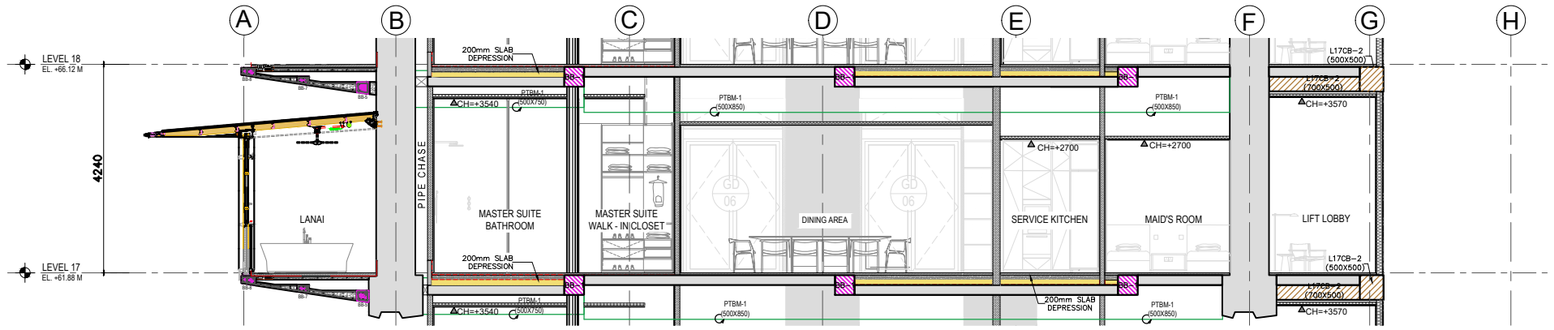

LEVEL 17
SECTION THRU-E
3 SD-1 SCALE 1:125M

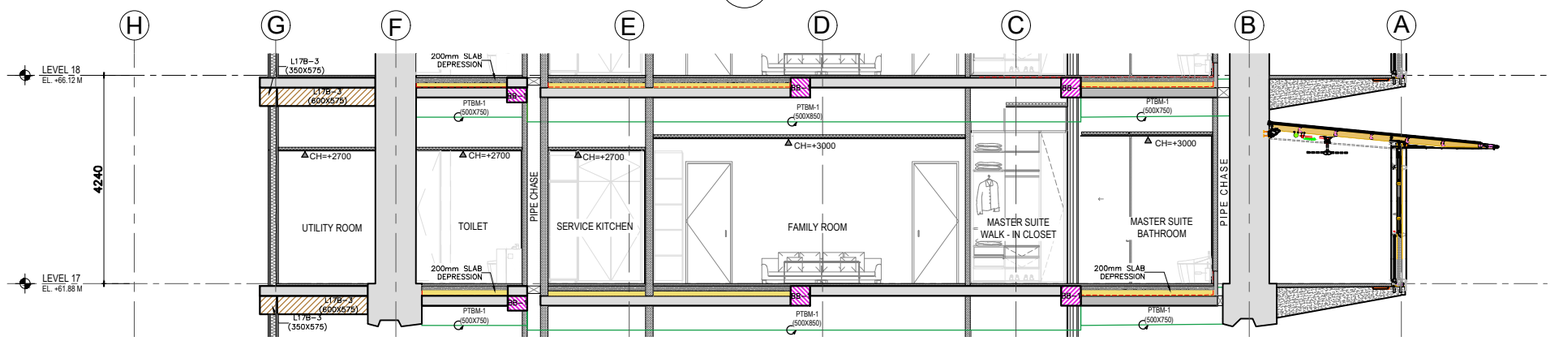

LEVEL 17
SECTION THRU-F
4 SD-1 SCALE 1:125M

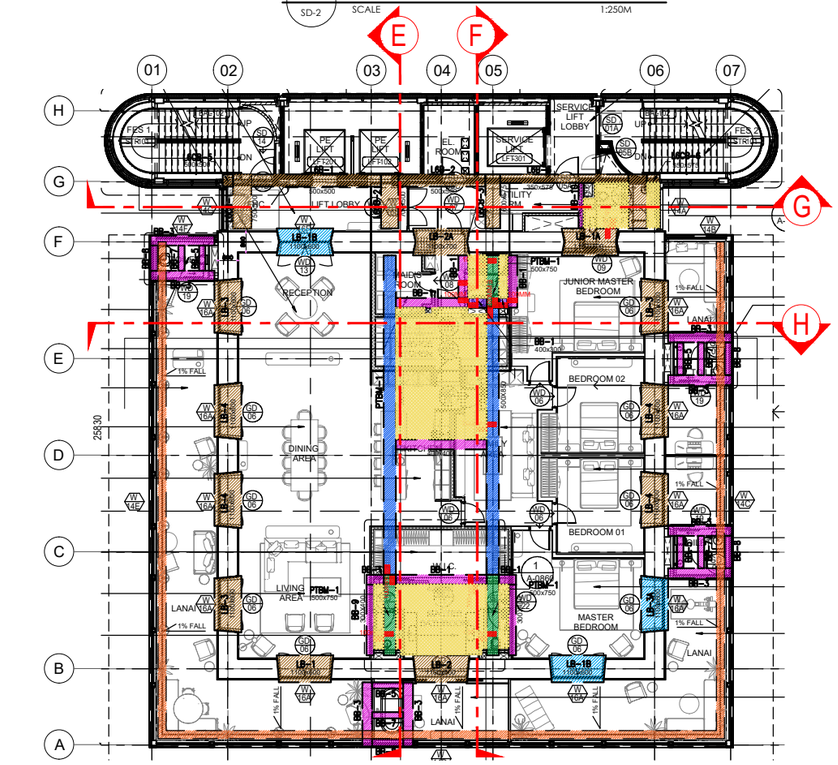

LEVEL 17
BODY PLAN
2 SD-2 SCALE 1:250M

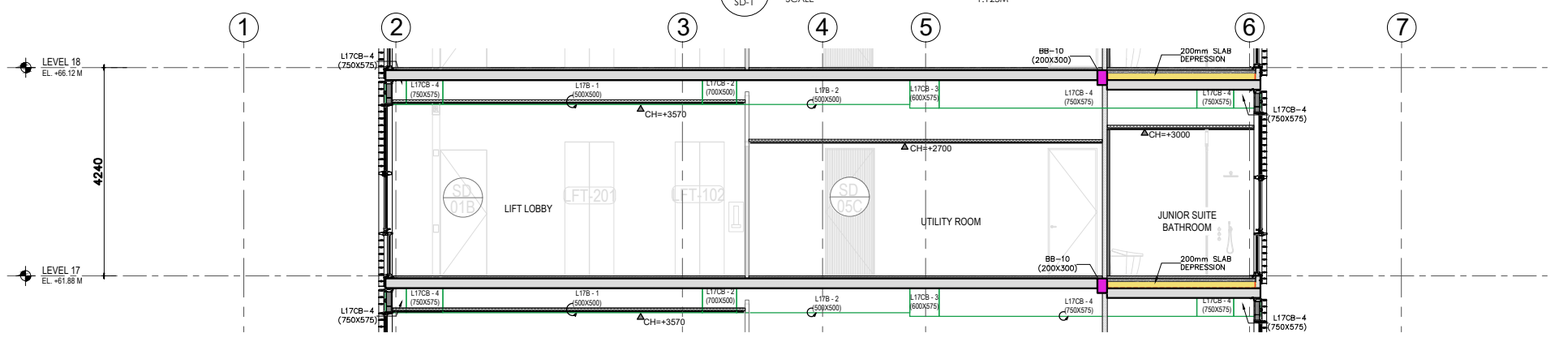

LEVEL 17
SECTION THRU-G
5 SD-1 SCALE 1:125M

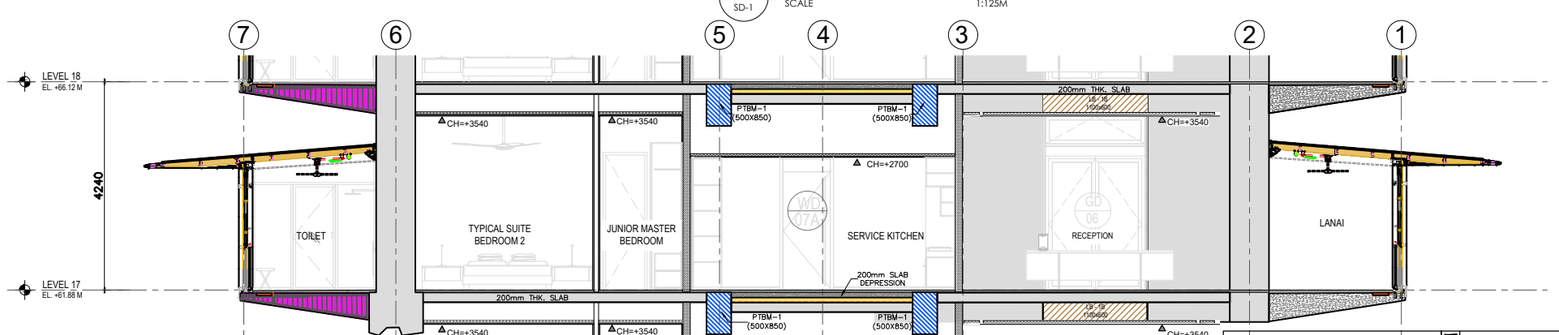

LEVEL 17
SECTION THRU-H
6 SD-1 SCALE 1:125M

KEY PLAN:

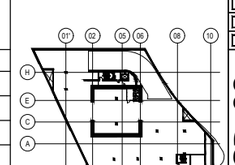

- ☐ ADVANCE COPY
- ☐ FOR REVIEW
- ☐ SUBMITTAL
- ☐ FOR IMPLEMENTATION

SHEET NO. CP-03 — SD 2

CONTRACTOR:	CAD BY:	MGPJR/MFLV	ARCHITECT:	STRUCTURAL:	OWNER/DEVELOPER:	PROJECT TITLE:	SHEET CONTENT:	REVISION:	DATE:
DDT KONSTRACT, INC. CONTRACTOR • ENGINEERS DDT Konstract, Inc. Unit 1206 12th Floor, The Olive Place, 622 Shaw Boulevard, Brgy. Addition Hills Mandaluyong City 1552. Philippines Tel: +632 8287 7888 Website: www.ddtkonstract.com	CHECKED BY:	MGPJR TSD HEAD	CASAS+ ARCHITECTS 8th FLOOR, PASEO CENTER, 8737 PASEO DE ROXAS AVENUE SALCEDO VILLAGE, MAKATI CITY 1227 PHILIPPINES TEL. NO. (+632) 8-840-0400 EMAIL: info@casasarchitects.com	SyC & ASSOCIATES STRUCTURAL CONSULTANTS SyC Campus, 3601, 1225 Kamagong, Makati City Telephone No. (+632) 8-893-0-55 Fax No. 8898/8782 to 85 Email Address: arcmnac@sfc.com.ph	Bonifacio West Development Corporation GROUND FLOOR MALL FORBES TOWN ROAD BONIFACIO GLOBAL CITY, TAGUIG CITY, PHILIPPINES	BWDC Residential Tower 26TH STREET CORNER FORBES TOWN ROAD, BONIFACIO GLOBAL CITY, TAGUIG CITY PHILIPPINES	LEVEL 17 1.RCP PLAN 2. BODY PLAN 3.SECTIONS		
	APPROVED BY:	JBTM PROJ. MNGR.	DESIGN CONSULTANT: Foster + Partners Riverside, 22 Hester Road, London SW11 4AN T:+44 (0)20 7738 0455 © Foster + Partners 2017	PROJECT MANAGER: design coordinates, inc. Suite 202, ITC Building, 337 San. Gil Puyat Avenue, Makati City, Philippines Telephone No. (+632) 8896 1981 to 84 Email: info@dci-corp.ph					
	DATE:	DECEMBER 2024							

DDTKI-OP-TSD-1.OA2 Landscape
Revision: 1